



A COMMUNITY OF CHOICE

Planning and Development Department

2101 O'Neil Avenue, Suite 202, Cheyenne WY 82001
(Phone) 307-637-6282 (Fax) 307-637-6366

MEMO

To: Honorable Mayor Patrick Collins and Members of the City Council
From: Connor White, Planner II
Subject: County Pocket Annexation #3
Date: November 12, 2024

Background:

The item for consideration is an Ordinance. Annexation of County pockets is a 2022 City Council priority. A "County pocket" is an area of unincorporated land 100% surrounded by the City of Cheyenne. A related "Assigned Zoning" pursuant to Unified Development Code (UDC) Section 2.2.8 ordinance is also on the agenda.

The proposed Governing Body review schedule is as follows:

- Introduction and referral: November 12, 2024
- Public Services Committee: November 19, 2024
- Second Reading: November 25, 2024
- Public Services Committee: December 3, 2024
- Third and Final Reading: December 9, 2024

This annexation is comprised of 38 properties 100% surrounded by the City (See attached map). Of the 38 parcels, 28 are developed with residential uses, one is developed with a commercial use, one is developed with a church and others are undeveloped or incorporated into adjacent parcels under similar ownership. The City has maintained contact with the County Planning Office to coordinate any pending permits or development reviews. Currently there are no active permits or development specific to the properties proposed for annexation.

On September 25, 2024, City staff mailed a courtesy notice by first class mail to all landowners included in this annexation area inviting them to a "Question and Answer" on Wednesday, October 9, 2024. Twenty people attended this meeting. Discussion, comments, and questions primarily surrounded the annexation component. During the meeting staff provided information regarding trash collection, snow plowing, water and sewer services and what to expect with the annexation.

The existing use of any property annexed, including any livestock use, will be allowed to continue as is as a nonconforming use. Nonconforming uses may continue until they are abandoned for a period of 12-months. Residents within pockets have been encouraged to complete a Land Use Documentation form detailing the existing use of the land for documentation purposes. At the time of drafting of this memo, one property owner within the area has completed a land use documentation form which is

attached. Providing a completed form is not required nor does it prohibit a property owner from making future claims that a use was pre-existing. The form is simply a tool to assist future City staff members to determine if a use was in existence at the time of annexation.

City-initiated annexations do not require an owner's signature. To initiate an annexation, the City must adopt a resolution certifying that the annexation complies with Wyoming State Statute § 15-1-402. After the City adopts this resolution, the annexation follows the typical schedule, including a public hearing and the approval of an Ordinance which annexes the land. The Governing Body adopted Resolution No. 6432 initiating this annexation on October 28, 2023.

As with any annexation, City services will be extended to service the land contained in the annexation. City utilities are already located in the vicinity. Police, fire, and sanitation services will be provided. As several parcels of land contained in this annexation area are developed, City sanitation service will need to be established and landowners have been notified of this required change. Infrastructure improvements required related to the annexation are minimal. Future development such as subdivision or new development will require on- and off-site infrastructure improvements. Existing infrastructure will remain as is upon annexation. All roads adjacent to annexed parcels are within City limits and maintained by the City.

The areas proposed for annexation are adjacent to land under City jurisdiction. Development in this area is a natural extension of the City. 100 % of the perimeter of the annexation area is contiguous to City limits.

Due to meeting the review criteria found in Wyoming Statute § 15-1-402 and the annexation conforming with the 2022 City Council goal to annex County pockets, staff recommends approval of this annexation.

Staff Recommendation:

Staff recommends the Governing Body approve the Annexation Ordinance.

Attachments:

1. Proposed Ordinance (includes Annexation Map as Attachment A)
2. Staff Report

ORDINANCE NO. _____

ENTITLED: "AN ORDINANCE ANNEXING TO THE CITY OF CHEYENNE, WYOMING, VARIOUS TRACTS OF LAND COMPLETELY SURROUNDED BY CURRENT CITY LIMITS SITUATE IN NORTHEAST CHEYENNE GENERALLY LOCATED NORTH OF BEVANS STREET, WEST OF COLLEGE DRIVE, AND SOUTH OF DELL RANGE BOULEVARD."

BE IT ORDAINED BY THE GOVERNING BODY OF THE CITY OF CHEYENNE, WYOMING:

Section 1. That the City of Cheyenne hereby finds as follows:

(a) That the City of Cheyenne has initiated this annexation in compliance with Wyo. Stat. § 15-1-404, and has adopted a Resolution certifying that the area to be annexed complies with the requirements of Wyo. Stat. § 15-1-402 (said resolution being adopted on October 28, 2024, as Resolution #6432);

(b) That an accurate legal description of said land is as follows:

Various tracts of land situate in northwest Cheyenne more particularly described as follows:

Area #1

PARCELS OF LAND SITUATE IN NW¼ NW¼, SECTION 27, T. 14 N., R. 66 W., 6TH P.M., LARAMIE COUNTY, WYOMING, BEING MORE PARTICULARLY DESCRIBED AS FOLLOWS:

Parcel #1 - SOUTH 320' OF THE NORTH 360' OF THE WEST 130' OF SAID SECTION 27

Parcel #2 - ALL OF LOTS 1-4, BLOCK 1, DARNELL HOMESITES.

Parcel #3 - ALL OF LOTS 1-4, BLOCK 2, DARNELL HOMESITES TOGETHER A THAT PORTION OF THE NW¼ NW¼, SECTION 27 LYING EAST OF RIDGE ROAD RIGHT-OF-WAY, SOUTH OF NORTHCREST, 2ND FILING, EAST OF NORTHCREST, 1ST FILING AND NORTH OF LOT 1, BLOCK 2, DARNELL HOMESITES. PARCEL DIMENSIONS ARE 200' EAST-WEST AND 320' NORTH-SOUTH.

SAID PARCELS CONTAIN 10.49 ACRES MORE OR LESS.

Area #2

PARCELS OF LAND SITUATE IN NW $\frac{1}{4}$ NW $\frac{1}{4}$, SECTION 27, T. 14 N., R. 66 W., 6TH P.M., LARAMIE COUNTY, WYOMING, BEING MORE PARTICULARLY DESCRIBED AS FOLLOWS:

PARCELS #4-5 - ALL OF THE SE $\frac{1}{4}$ NW $\frac{1}{4}$ NW $\frac{1}{4}$ OF SAID SECTION 27
- ALL OF THE SE $\frac{1}{4}$ NW $\frac{1}{4}$ NW $\frac{1}{4}$ OF SAID SECTION 27 EXCEPTING
THEREFROM DRY CREEK PARKWAY, 2ND FILING.

SAID PARCELS CONTAIN 8.23 ACRES MORE OR LESS.

Area #3

PARCELS OF LAND SITUATE IN NW $\frac{1}{4}$ NW $\frac{1}{4}$, SECTION 27, T. 14 N., R. 66 W., 6TH P.M., LARAMIE COUNTY, WYOMING, BEING MORE PARTICULARLY DESCRIBED AS FOLLOWS:

PARCELS #6 - ALL OF LOTS 1-8, BLOCK 1, DOWNEY
SUBDIVISION.
PARCELS #7 - ALL OF LOTS 9-10, BLOCK 1, DOWNEY
SUBDIVISION.
PARCELS #8 - ALL OF LOTS 13-15, BLOCK 1, DOWNEY
SUBDIVISION.
PARCELS #9 - ALL OF LOTS 7-8, BLOCK 2, DOWNEY
SUBDIVISION.
PARCELS #10 - ALL OF LOTS 3-4, BLOCK 2, DOWNEY
SUBDIVISION.

SAID PARCELS CONTAIN 3.37 ACRES MORE OR LESS.

Area #4

PARCELS OF LAND SITUATE IN SE $\frac{1}{4}$ NW $\frac{1}{4}$, SECTION 27, T. 14 N., R. 66 W., 6TH P.M., LARAMIE COUNTY, WYOMING, BEING MORE PARTICULARLY DESCRIBED AS FOLLOWS:

PARCELS #11 - ALL OF LOTS 5-9, BLOCK 1, COULSON ADDITION.

PARCELS #12 - THE WEST 60 FEET OF THE EAST 180 FEET OF THE
SOUTH 120 FEET, TRACT 336, SUNNYSIDE ADDITION, 7TH
FILING.

PARCELS #13 - THE EAST 60 FEET OF THE SOUTH 120 FEET,
TRACT 336, SUNNYSIDE ADDITION, 7TH FILING TOGETHER
WITH A PORTION OF TRACT 6, BLOCK 2, COULSON ADDITION

DESCRIBED AS BEGINNING AT THE SOUTHWEST CORNER OF SAID LOT 6, THENCE 00°19'20" A DISTANCE OF 126.80 FEET; THENCE 90°26'01" A DISTANCE OF 39.74 FEET; THENCE 184°34'39" A DISTANCE OF 135.185 FEET; THENCE 270°28'12" A DISTANCE OF 29.71 FEET TO THE POINT OF BEGINNING.

PARCELS #14 - THE SOUTH 126.82 FEET OF LOT 1, BLOCK 1, RODGERS SUBDIVISION LYING SOUTH OF THE VACATED 16 FOOT ALLEY.

SAID PARCELS CONTAIN 1.62 ACRES MORE OR LESS.

Area #5

PARCELS OF LAND SITUATE IN NW¼ SW¼, SECTION 27, T. 14 N., R. 66 W., 6TH P.M., LARAMIE COUNTY, WYOMING, BEING MORE PARTICULARLY DESCRIBED AS FOLLOWS:

PARCELS #15 - THE NORTH 209.45 FEET OF TRACTS 201-204, SUNNYSIDE ADDITION, 6TH FILING EXCEPTING THEREFROM THE EAST 10.00 FEET OF THE NORTH 209.45 OF TRACT 204, SUNNYSIDE ADDITION, 6TH FILING.

SAID PARCELS CONTAIN 2.96 ACRES MORE OR LESS.

- (c) That the annexation of said area is for the protection of health, safety, and welfare of the persons residing in the area and the City of Cheyenne;
- (d) That the urban development of the area sought to be annexed will constitute a natural, geographical, economical and social part of the City of Cheyenne;
- (e) That the area is a logical and feasible addition to the City and that the extension of basic services such as water and sewer systems, police and fire protection and other services customarily available in the City of Cheyenne can, within reason, be furnished;
- (f) That the area is considered contiguous to the City of Cheyenne according to the provisions of Wyo. Stat. § 15-1-402 (b) and is currently zoned MR Medium-density Residential, HR High-density Residential and PUD Planned Unit Development by the Laramie County Commissioners; and
- (g) That the City of Cheyenne does not own or operate its own electrical utility, and its governing body is prepared to designate a utility to serve the annexed area pursuant to Wyo. Stat. § 15-1-410, and to authorize the designated utility to serve the entire annexed area.

Section 2. That all of the real property described in Section 1(b) of this Ordinance is hereby annexed to the City of Cheyenne, Wyoming, and shall become a part thereof.

Section 3. That pursuant to Wyoming Statute § 15-1-405, the Governing Body held a public hearing on November 12, 2024, on the proposed annexation and found that the annexation complied Wyo. Stat. § 15-1-402.

Section 4. That the map of the area to be annexed is shown in Exhibit A, which is attached hereto and incorporated herein, satisfies the requirements of Wyo. Stat. § 15-1-406 and shall be recorded with the county clerk in conjunction with this ordinance.

Section 5. That the City Clerk is directed to file an executed copy of this annexation ordinance with the County Clerk and Ex-Officio Register of Deeds for Laramie County, Wyoming, and shall also notify the City Engineer's Office to add said area to the official City Map of the City of Cheyenne, Wyoming.

Section 6. Sections, paragraphs, sentences, clauses and phrases of this ordinance are severable. If any phrase, clause, sentence, paragraph or section of this ordinance is declared illegal or unconstitutional, such illegality or unconstitutionality shall not affect any of the remaining phrases, clauses, sentences, paragraphs and sections.

Section 7. That this ordinance shall be in full force and effect upon its publication.

FIRST READING: _____

SECOND READING: _____

THIRD AND FINAL READING: _____

PATRICK COLLINS, MAYOR

(SEAL)

ATTEST:


KRISTINA F. JONES, CITY CLERK

Published: _____
Wyoming Tribune-Eagle

(EXHIBIT "A")
**ANNEXATION MAPS FOR
VARIOUS COUNTY POCKETS SITUATE IN THE WEST 1/2 OF
SECTION 27, T. 14 N., R. 66 W., 6TH P.M.,
CITY OF CHEYENNE, LARAMIE COUNTY, WYOMING**




VICINITY MAP
NOT TO SCALE

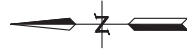

FILING RECORD

AZIMUTH

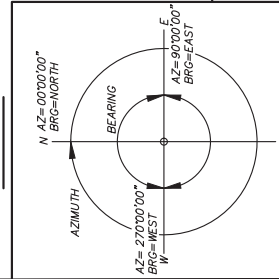

APPROVALS

APPROVED BY THE CITY COUNCIL OF THE CITY OF CHEYENNE, WYOMING, THIS
____ DAY OF _____, 2024.


MAYOR – PATRICK COLLINS _____
CITY CLERK – KRISTINA F. JONES _____

NOTES

1. DISTANCES SHOWN ON THE ANNEXATION MAP ARE GROUND DISTANCE.
2. THE AREA WITHIN THE HEAVY BOUNDARY IS CURRENTLY A COUNTY POCKET. ALL AREAS OUTSIDE THE BOUNDARY ARE WITHIN THE LIMITS OF THE CITY OF CHEYENNE.
3. LENGTH OF THE PARCEL BOUNDARY ABUTTING THE CITY LIMITS – 23,726' (ALL SIDES OF THE PARCELS AS SHOWN ARE BOUNDED BY THE CITY LIMITS.
4. RATIO OF THE BOUNDARY ABUTTING THE CITY LIMITS – 100% OF THE TOTAL
5. CERTAIN POCKET PARCELS ARE DEPICTED FROM MAPS, PLATS AND DEEDS OF RECORD AND WERE NOT DETERMINED FROM ACTUAL FIELD SURVEYS.

SURVEYORS CERTIFICATE

I, COTTON D. JONES, A REGISTERED PROFESSIONAL LAND SURVEYOR IN THE STATE OF WYOMING, HEREBY STATE THAT THESE ANNEXATION MAPS WERE PREPARED FROM OFFICIAL PLATS AND DEEDS OF RECORD AND/OR FROM NOTES OF A FIELD SURVEY CONDUCTED BY MYSELF AND UNDER MY DIRECT SUPERVISION DURING THE MONTHS OF MAY–JUNE, 2024, THAT THE MONUMENTS ARE SET OR FOUND AS SHOWN AND THAT THESE MAPS CORRECTLY REPRESENT SAID SURVEYS AND MAP AND DEED DESCRIPTIONS OF THE LANDS DEPICTED HEREON TO THE BEST OF MY KNOWLEDGE.

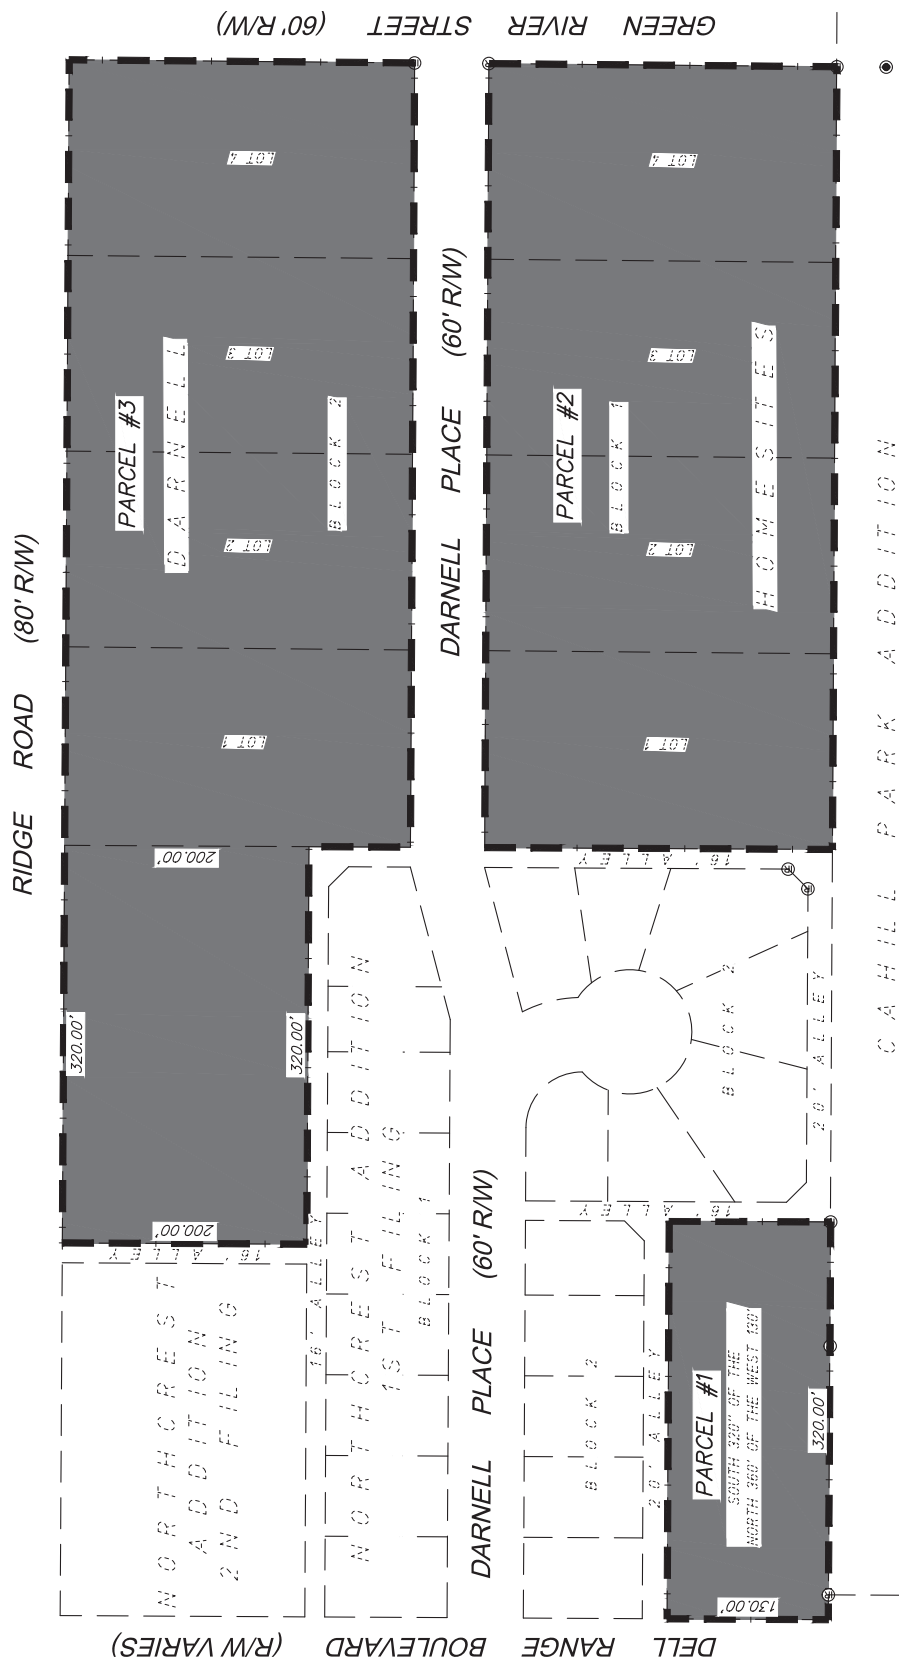

- LEGEND**
- PROPOSED AREA FOR ANNEXATION
 - EXISTING CITY LIMITS
 - FOUND 1" PLASTIC CAP
 - FOUND STANDARD WYDOT RIGHT-OF-WAY MONUMENT
 - FOUND ALUMINUM CAP
 - FOUND #5 REBAR

LAND DESCRIPTION

PARCELS OF LAND SITUATE IN NW¼ NW¼, SECTION 27, T. 14 N., R. 66 W., 6TH P.M., LARAMIE COUNTY, WYOMING, BEING MORE PARTICULARLY DESCRIBED AS FOLLOWS:


PARCEL #1 — SOUTH 320' OF THE NORTH 360' OF THE WEST 130' OF SAID SECTION 27

PARCEL #2 — ALL OF LOTS 1-4, BLOCK 1, DARNELL HOMESITES.


PARCEL #3 — ALL OF LOTS 1-4, BLOCK 2, DARNELL HOMESITES TOGETHER A THAT PORTION OF THE NW¼ NW¼, SECTION 27 LYING EAST OF RIDGE ROAD RIGHT-OF-WAY, SOUTH OF NORTHCREST, 2ND FILING, EAST OF NORTHCREST, 1ST FILING AND NORTH OF LOT 1, BLOCK 2, DARNELL HOMESITES. PARCEL DIMENSIONS ARE 200' EAST-WEST AND 320' NORTH-SOUTH.


SAID PARCELS CONTAIN 10.49 ACRES MORE OR LESS.

AZIMUTH

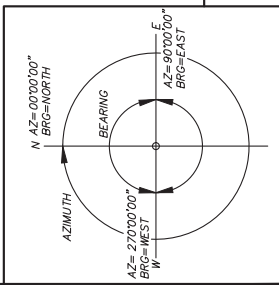

FILING RECORD

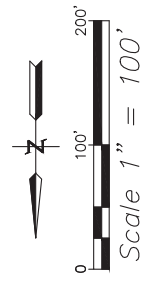

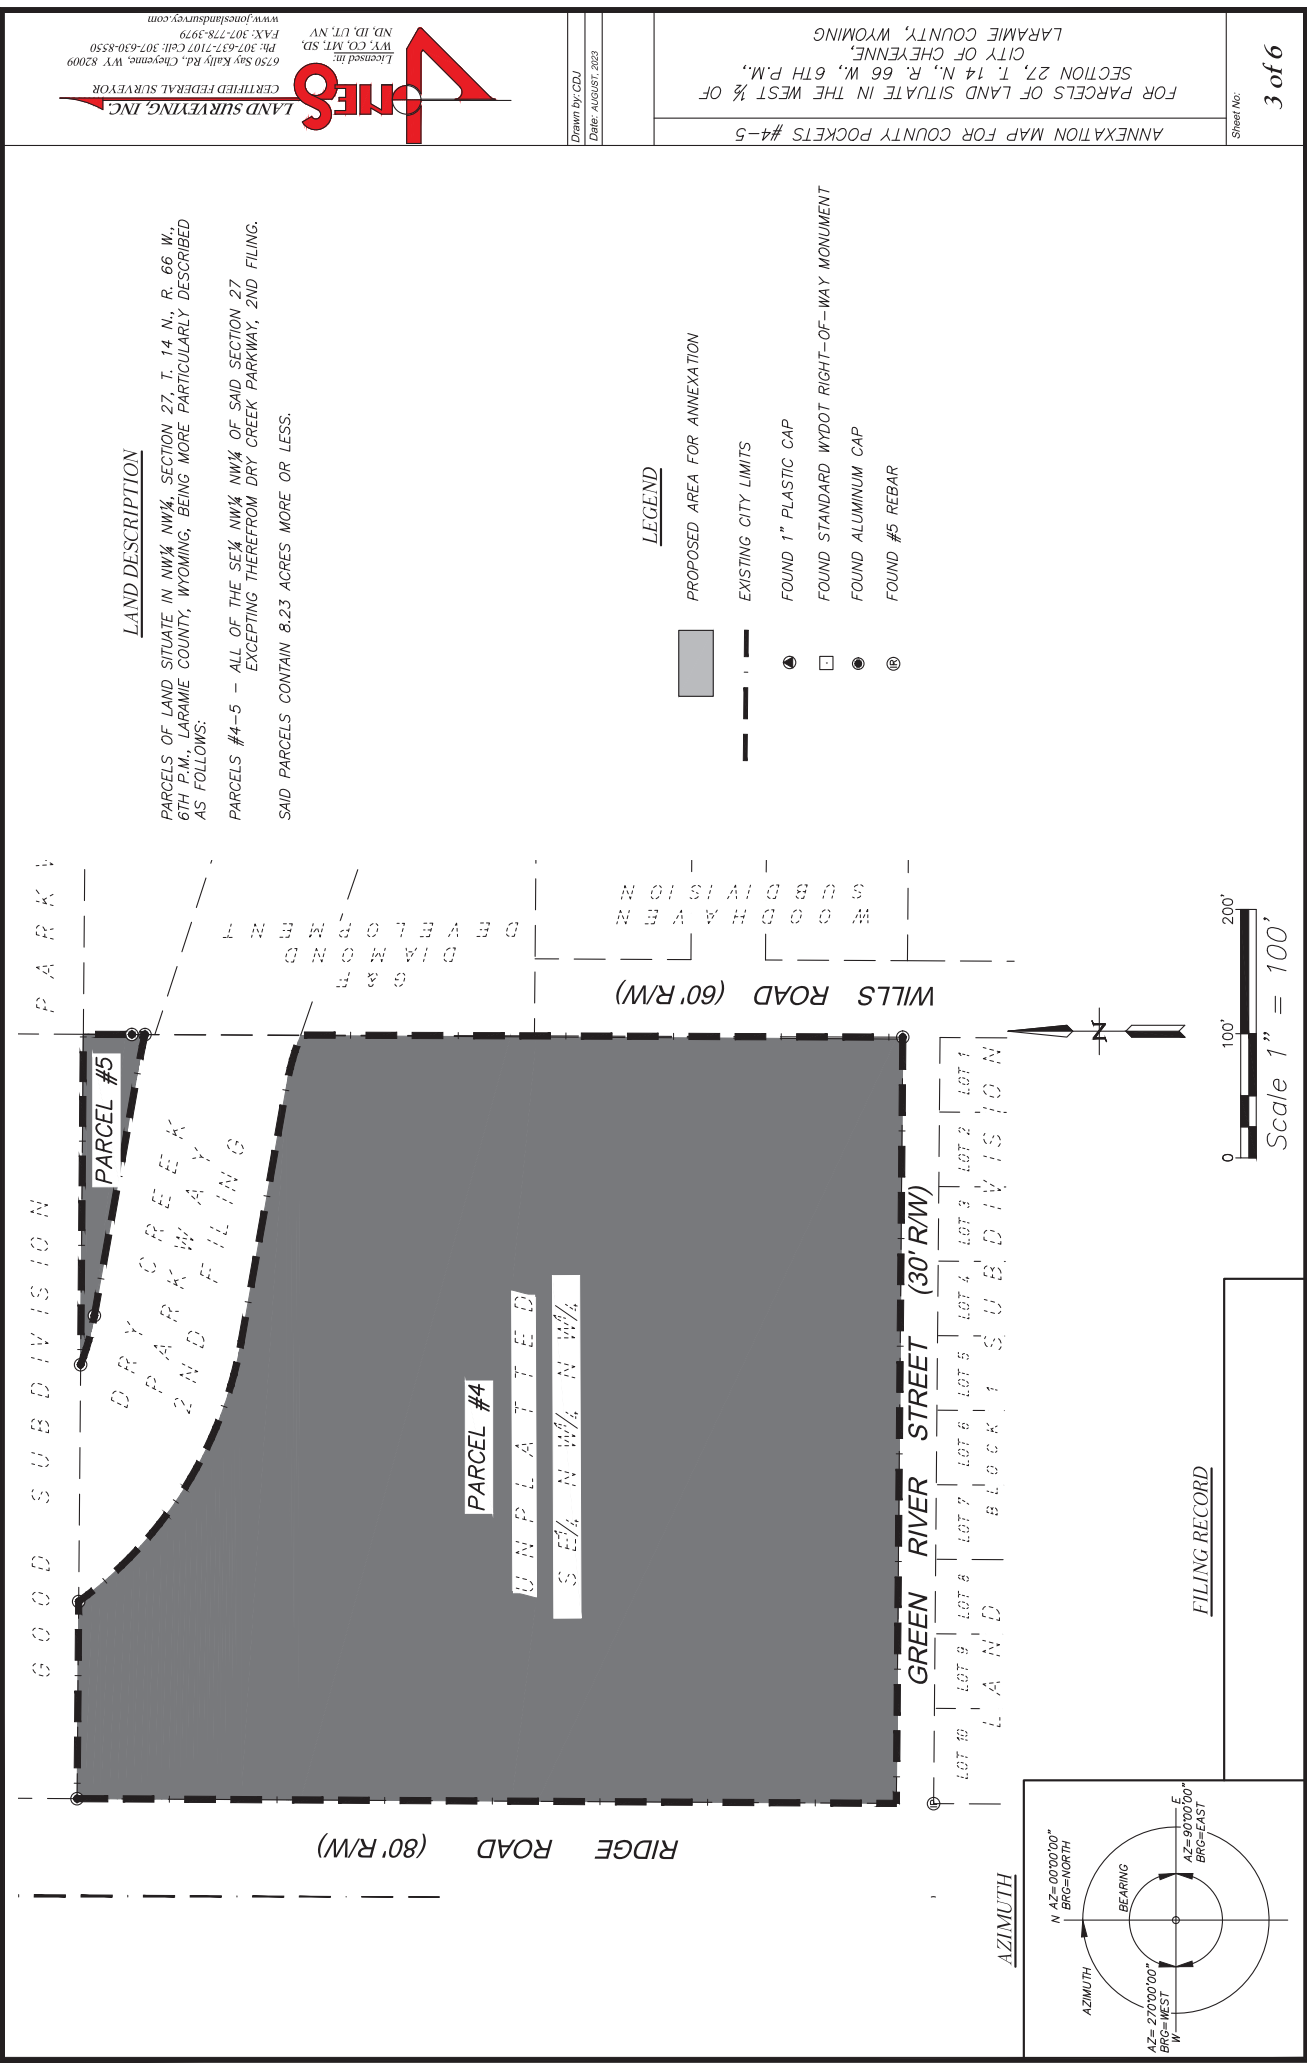

LAND DESCRIPTION



PARCELS OF LAND SITUATE IN NW¼ NW¼, SECTION 27, T. 14 N., R. 66 W., 6TH P.M., LARAMIE COUNTY, WYOMING, BEING MORE PARTICULARLY DESCRIBED AS FOLLOWS:

PARCELS #4-5 - ALL OF THE SE¼ NW¼ NW¼ OF SAID SECTION 27 EXCEPTING THEREFROM DRY CREEK PARKWAY, 2ND FILING.

SAID PARCELS CONTAIN 8.23 ACRES MORE OR LESS.

LEGEND

- PROPOSED AREA FOR ANNEXATION
- EXISTING CITY LIMITS
- FOUND 1" PLASTIC CAP
- FOUND STANDARD WYDOT RIGHT-OF-WAY MONUMENT
- FOUND ALUMINUM CAP
- FOUND #5 REBAR

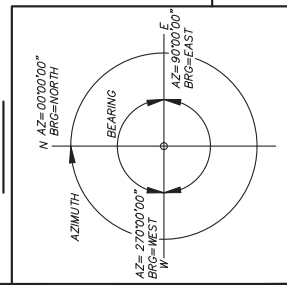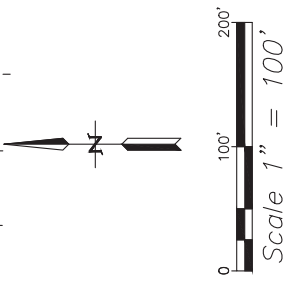

FILING RECORD

4

ONES

LAND SURVEYING, INC.

CERTIFIED FEDERAL SURVEYOR

6750 Sky Kally Rd., Cheyenne, WY 82009

Ph: 307-637-7107 Cell: 307-630-8550

FAX: 307-778-3979

www.jonessurveysurvey.com


Licensed In

WY, CO, MT, SD,


ND, ID, UT, NV

Drawn by: CDJ
Date: AUGUST, 2023


ANNEXATION MAP FOR COUNTY POCKETS #4-5
FOR PARCELS OF LAND SITUATE IN THE WEST ½ OF SECTION 27, T. 14 N., R. 66 W., 6TH P.M., LARAMIE COUNTY, WYOMING

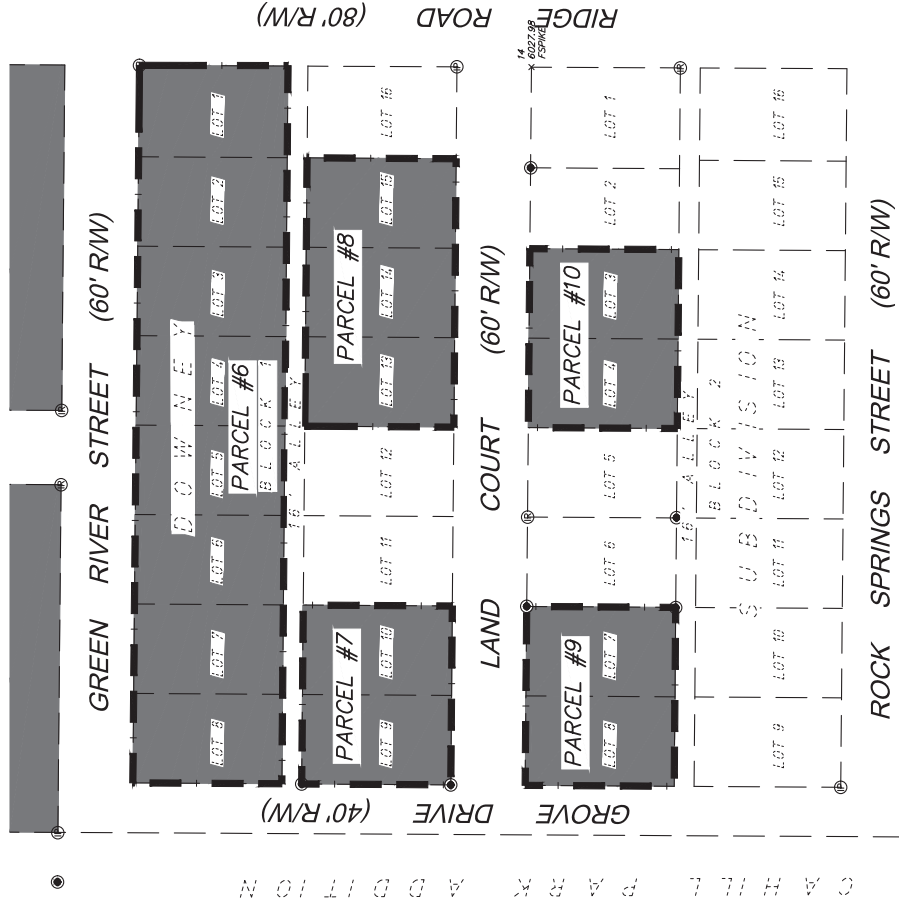

AZIMUTH

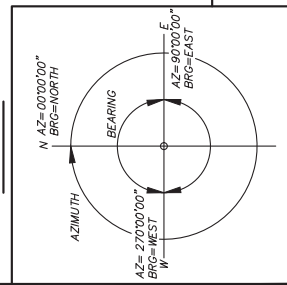

FILING RECORD

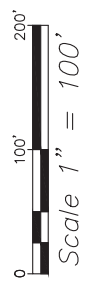

LAND DESCRIPTIONS

PARCELS OF LAND SITUATE IN NW¼ NW¼, SECTION 27, T. 14 N., R. 66 W., 6TH P.M., LARAMIE COUNTY, WYOMING, BEING MORE PARTICULARLY DESCRIBED AS FOLLOWS:

PARCELS #6 – ALL OF LOTS 1–8, BLOCK 1, DOWNEY SUBDIVISION.

PARCELS #7 – ALL OF LOTS 9–10, BLOCK 1, DOWNEY SUBDIVISION.

PARCELS #8 – ALL OF LOTS 13–15, BLOCK 1, DOWNEY SUBDIVISION.

PARCELS #9 – ALL OF LOTS 7–8, BLOCK 2, DOWNEY SUBDIVISION.

PARCELS #10 – ALL OF LOTS 3–4, BLOCK 2, DOWNEY SUBDIVISION.


SAID PARCELS CONTAIN 3.37 ACRES MORE OR LESS.

LEGEND



- PROPOSED AREA FOR ANNEXATION
- EXISTING CITY LIMITS
- FOUND 1" PLASTIC CAP
- FOUND STANDARD WYDOT RIGHT-OF-WAY MONUMENT
- FOUND ALUMINUM CAP
- FOUND #5 REBAR



RAWLINS STREET (60' R/W)

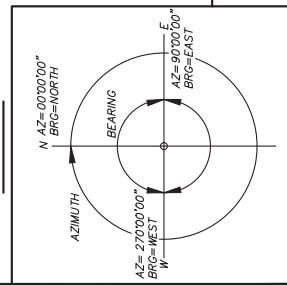

FILING RECORD

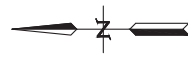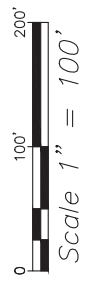

LAND DESCRIPTION

PARCELS OF LAND SITUATE IN SE¼ NW¼, SECTION 27, T. 14 N., R. 66 W., 6TH P.M., LARAMIE COUNTY, WYOMING, BEING MORE PARTICULARLY DESCRIBED AS FOLLOWS:

PARCELS #11 – ALL OF LOTS 5–9, BLOCK 1, COULSON ADDITION.

PARCELS #12 – THE WEST 60 FEET OF THE EAST 180 FEET OF THE SOUTH 120 FEET, TRACT 336, SUNNYSIDE ADDITION, 7TH FILING.


PARCELS #13 – THE EAST 60 FEET OF THE SOUTH 120 FEET, TRACT 336, SUNNYSIDE ADDITION, 7TH FILING TOGETHER WITH A PORTION OF TRACT 6, BLOCK 2, COULSON ADDITION DESCRIBED AS BEGINNING AT THE SOUTHWEST CORNER OF SAID LOT 6, THENCE 00°19'20" A DISTANCE OF 126.80 FEET; THENCE OF 90°26'01" A DISTANCE OF 39.74 FEET; THENCE 184°34'39" A DISTANCE OF 135.185 FEET; THENCE 270°28'12" A DISTANCE OF 29.71 FEET TO THE POINT OF BEGINNING.

PARCELS #14 – THE SOUTH 126.82 FEET OF LOT 1, BLOCK 1, RODGERS SUBDIVISION LYING SOUTH OF THE VACATED 16 FOOT ALLEY.

SAID PARCELS CONTAIN 1.62 ACRES MORE OR LESS.

LEGEND

- PROPOSED AREA FOR ANNEXATION
- EXISTING CITY LIMITS
- FOUND 1" PLASTIC CAP
- FOUND STANDARD WYDOT RIGHT-OF-WAY MONUMENT
- FOUND ALUMINUM CAP
- FOUND #5 REBAR

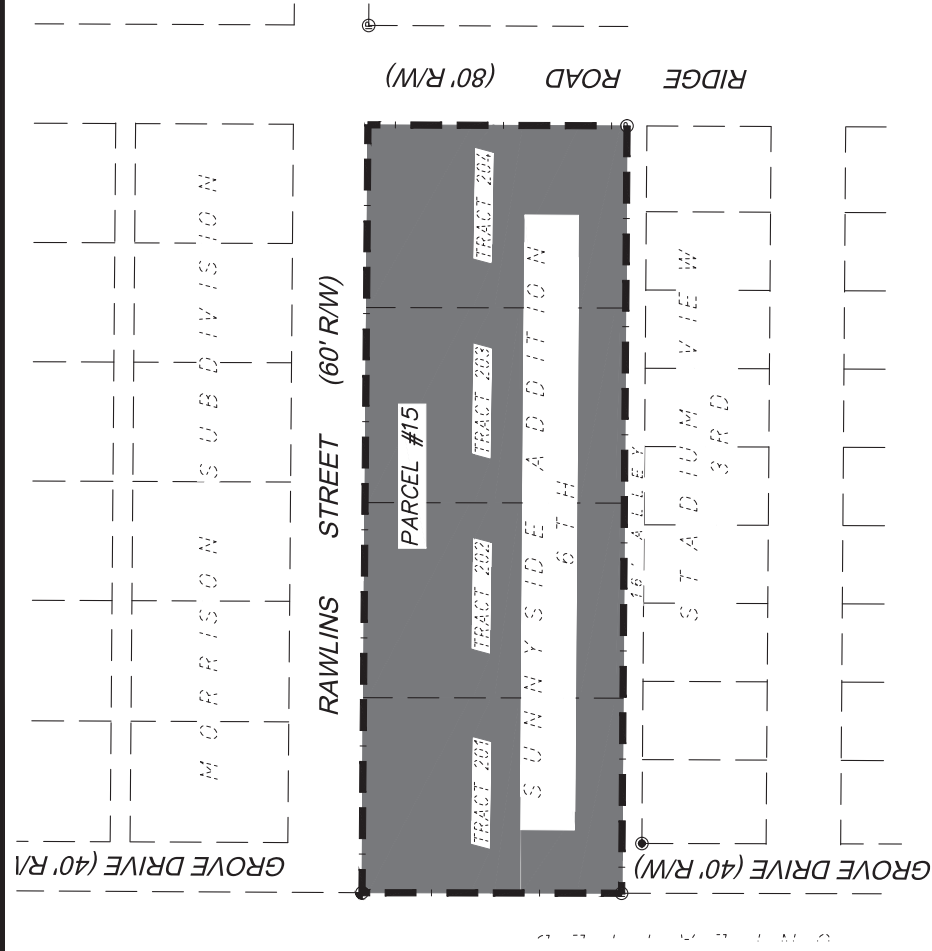

LAND DESCRIPTION

PARCELS OF LAND SITUATE IN NW¼ SW¼, SECTION 27, T. 14 N., R. 66 W., 6TH P.M., LARAMIE COUNTY, WYOMING, BEING MORE PARTICULARLY DESCRIBED AS FOLLOWS:

PARCELS #15 - THE NORTH 209.45 FEET OF TRACTS 201-204, SUNNYSIDE ADDITION, 6TH FILING EXCEPTING THEREFROM THE EAST 10.00 FEET OF THE NORTH 209.45 OF TRACT 204, SUNNYSIDE ADDITION, 6TH FILING.

SAID PARCELS CONTAIN 2.96 ACRES MORE OR LESS.

LEGEND

PROPOSED AREA FOR ANNEXATION

EXISTING CITY LIMITS


FOUND 1" PLASTIC CAP

FOUND STANDARD WYDOT RIGHT-OF-WAY MONUMENT


FOUND ALUMINUM CAP

FOUND #5 REBAR

AZIMUTH

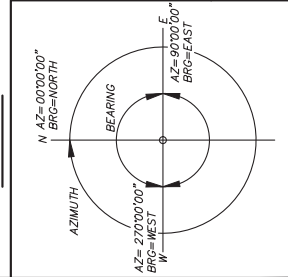

FILING RECORD

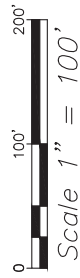



A COMMUNITY OF CHOICE

Planning and Development Department
2101 O'Neil Avenue, Suite 202, Cheyenne WY 82001
(Phone) 307-637-6282 (Fax) 307-637-6366

CITY OF CHEYENNE GOVERNING BODY
NOVEMBER 12, 2024
STAFF REPORT

FILE: PUDC-24-188: County Pocket #3 - Annexation

REQUEST: An annexation of 38 properties 100% surrounded by the City.

LOCATION: North of Bevans Street, west of College Drive, and south of Dell Range Boulevard.

PURPOSE: Annexation of County pockets is a 2022 City Council priority.

PREPARED BY: Connor White, Planner II



APPLICABLE CITY CODE SECTION(S) AND PLANS:

- UDC 2.4.2 Annexations
- PlanCheyenne

BACKGROUND:

Annexation of County pockets is a 2022 City Council priority. A “County pocket” is an area of unincorporated land 100% surrounded by the City of Cheyenne. City-initiated annexations do not require an owner’s signature. To initiate an annexation, the City must adopt a resolution certifying that the annexation complies with Wyoming State Statute § 15-1-402. After the City adopts this resolution, the annexation follows the typical schedule, including a public hearing and the approval of an Ordinance which annexes the land. The Governing Body adopted Resolution No. 6432 initiating this annexation on October 28, 2023.

This annexation is comprised of 38 properties 100% surrounded by the City (See attached map). Of the 38 parcels, 28 are developed with residential uses, one is developed with a commercial use, one is developed with a church and others are undeveloped or incorporated into adjacent parcels under similar ownership.

Land annexed to the City requires a City zone. An assigned zoning ordinance is accompanying this annexation to assign the MR, HR and CB zones.

ANALYSIS OF APPLICATION CONFORMANCE WITH REVIEW CRITERIA:

To approve the annexation Ordinance, the Governing Body must make the following findings required in WS 15-1-402; a detailed analysis of which is below:

1) An annexation of the area is for the protection of the health, safety and welfare of the persons residing in the area and in the city or town. [WS 15-1-402 (a) (i)]

The annexation of these properties will increase the health, safety, and welfare of the future occupants. By being in City limits, the property will receive access to City Fire and Police and sanitation services. The properties will also have the option of connecting to City water and sanitary sewer instead of having wells and septic systems.

The application **complies** with this review criterion.

2) The urban development of the area sought to be annexed would constitute a natural, geographical, economical and social part of the annexing city or town. [WS 15-1-402 (a) (ii)]

These properties constitute a natural, geographic, economic, and social part of the city. The properties are surrounded by City on all sides. The contiguity to the City and the proximity to surrounding urban-style development makes the parcels a natural geographic part of the City.

The application **complies** with this review criterion.

- 3) The area sought to be annexed is a logical and feasible addition to the annexing city or town and the extension of basic and other services customarily available to residents of the city or town shall, within reason, be available to the area proposed to be annexed. [WS 15-1-402 (a) (iii)]**

The area is a logical and feasible addition to the City due to the reasons previously listed. All City services normally available to residents will also be made available. Police and fire protection will be extended upon annexation. Utilities exist in the area and will be expanded into the proposed area as they redevelop.

The application **complies** with this review criterion.

- 4) The area sought to be annexed is contiguous with or adjacent to the annexing city or town, or the area meets the requirements of W.S. 15-1-407. [WS 15-1-402 (a) (iv)]**

The area proposed for annexation is 100% contiguous on all sides.

The application **complies** with this review criterion.

- 5) If the city or town does not own or operate its own electric utility, its governing body is prepared to issue one (1) or more franchises as necessary to serve the annexed area pursuant to W.S. 15-1-410. [WS 15-1-402 (a) (v)]**

Utility franchises are in place to serve the annexed area.

The application **complies** with this review criterion.

- 6) The annexing city or town, not less than twenty (20) business days prior to the public hearing required by W.S. 15-1-405(a), has sent by certified mail to all landowners and affected public utilities within the territory and by first class mail to any persons owning property that is adjacent to or within three hundred (300) feet of the territory proposed to be annexed, regardless of whether the property is inside or outside the corporate limits of the annexing city or town and regardless of whether the city or town is exercising authority under W.S. 15-3-202(b)(ii), a summary of the proposed annexation report as required under subsection (c) of this section and notice of the time, date and location of the public hearing required by W.S. 15-1-405(a). [WS 15-1-402 (a) (vi)]**

A certified mailing was made to the landowners and public utilities on October 10, 2024. Neighbors within 300' were mailed first-class letters the same day. The public hearing for this annexation is scheduled for November 12, 2024. Twenty (20) business days (on the City's calendar) prior to the announced public hearing is October 14, 2024. The earliest confirmation of delivery was dated October 11, 2024.

The application **complies** with this review criterion.

CONFORMANCE WITH APPLICABLE PLANS:

The project is located in an area covered by the following plans:

- Plan Cheyenne

The Future Land Use Map of PlanCheyenne, as updated by Connect 2045, anticipates this area of the community to develop with urban residential uses and a little bit of Mixed-use Residential uses. These areas are expected to develop with full access to urban services – such areas are best served by being within City limits. The area is within the Urban Service Boundary.

STAFF REVIEW:

Through the review process, no comments were received.

CONCLUSION:

Staff is satisfied that the application meets the review criteria and therefore recommends approval of the annexation.



The proposed annexation is a natural extension of the City, is contiguous to the current City limits, and most services typically available to urban areas are available to be extended to this property.

STAFF RECOMMENDATION:

Staff recommends approval of the annexation of the property.

ATTACHMENTS:

1. Current Zoning Map
2. Future Land Use Map
3. Annexation map

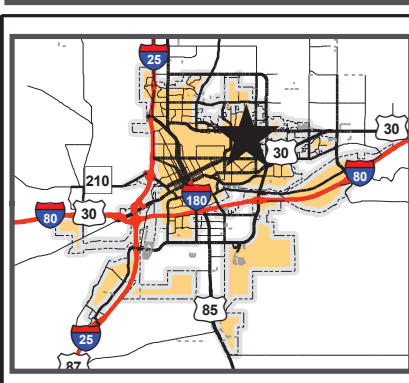
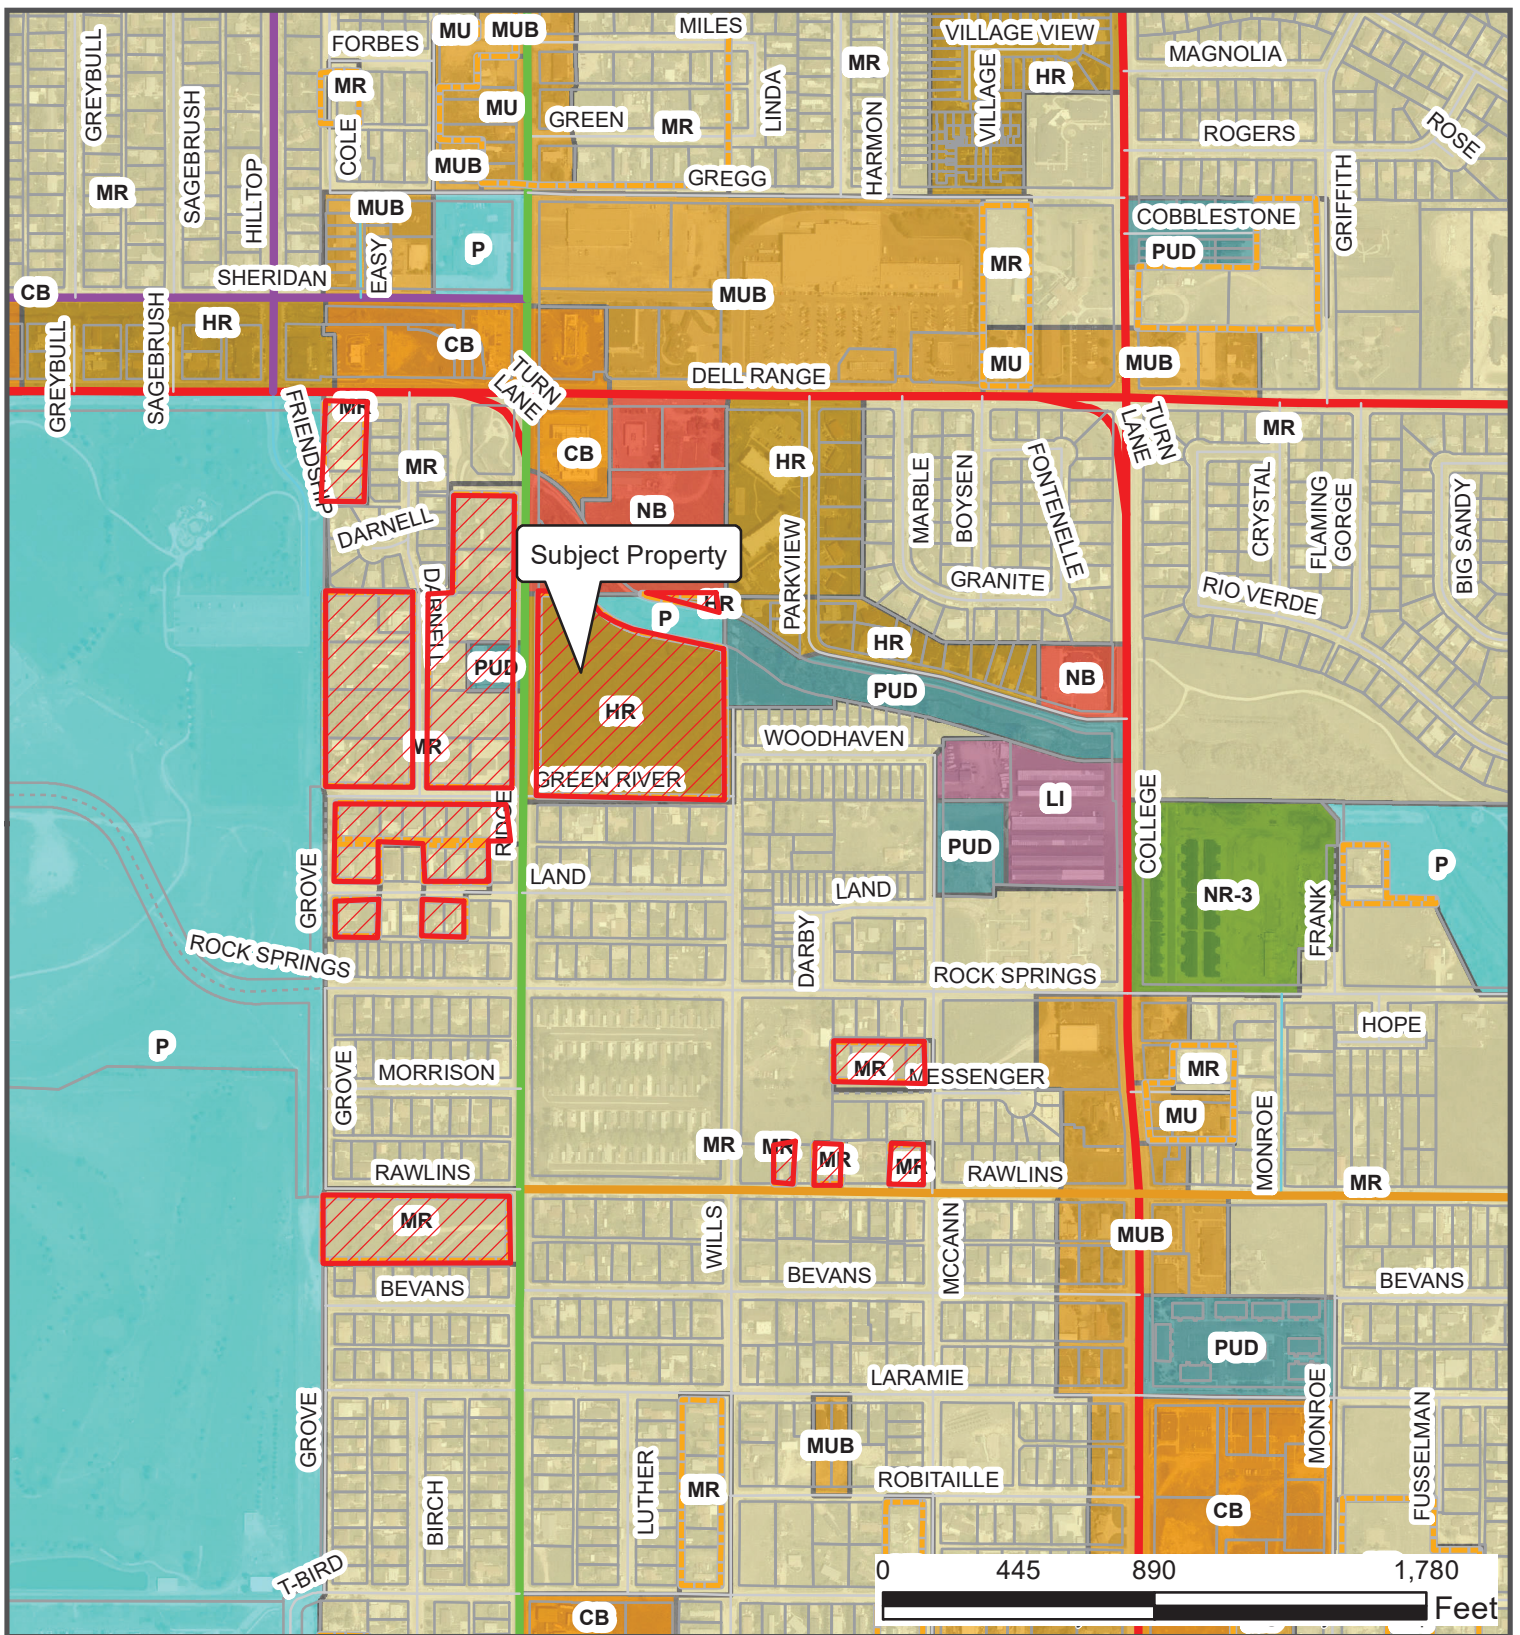


Attachment 1: Zoning Map PUDC-24-188

This map/data is made possible through the Cheyenne and Laramie County Cooperative GIS (CLCCGIS) Program and is for display purposes only. The CLCCGIS invokes its sovereign and governmental immunity in allowing access to or use of this data, makes no warranties as to the validity, and assumes no liability associated with the use or misuse of this information.

Legend

	Nov19_CityLimits		A-1 / Agricultural and Rural Residential
	Interstate		A-2 / Agricultural
	Principal Arterial		AG / City Agricultural
	Minor Arterial		MUR / Mixed Use Residential Emphasis
	Major Collector		CBD / Central Business District
	Minor Collector		CB / Community Business
	Local		NB / Neighborhood Business
	Private		MU / Mixed Use - County
	Platted not built		MUB / Mixed Use Business Emphasis
	HR / High Density Residential		MUE / Mixed Use Employment Emphasis
	MR / Medium Density Residential		HI / Heavy Industrial
	LR / Low Density Residential		LI / Light Industrial
	NR-2 / Neighborhood Residential - Med. Density		P / Public
	NR-3 / Neighborhood Residential - High Density		AD / Airport District
	AR / Agricultural Residential		PUD / Planned Unit Development
			X / Exempt

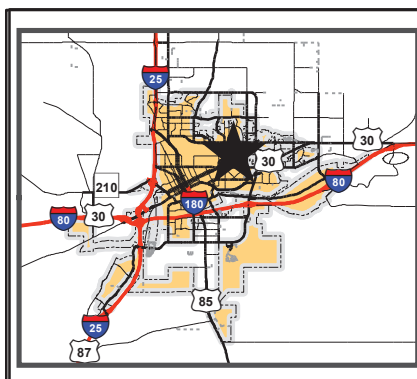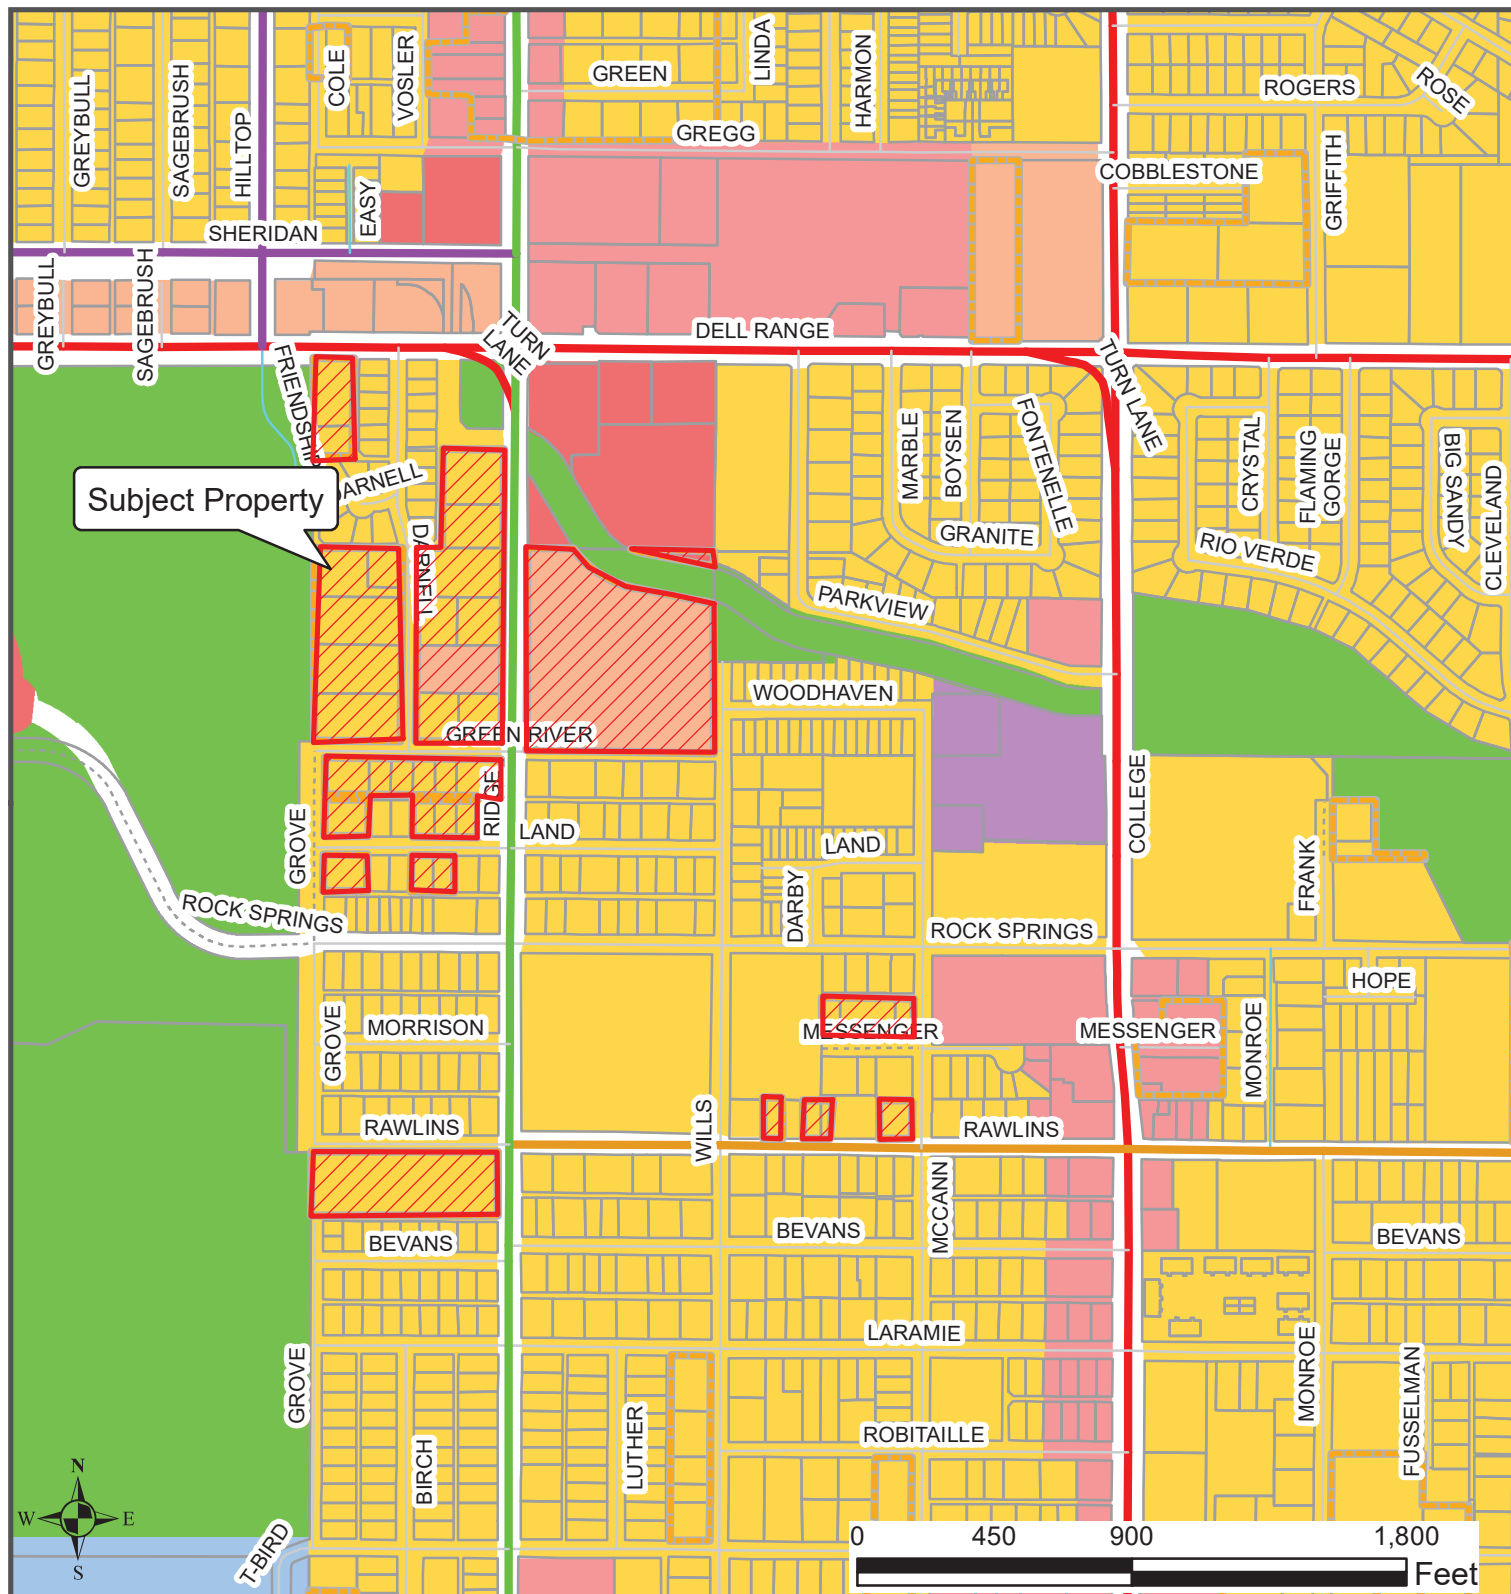

Attachment 2: Land Use Map PUDC-24-188

This map/data is made possible through the Cheyenne and Laramie County Cooperative GIS (CLCCGIS) Program and is for display purposes only. The CLCCGIS invokes its sovereign and governmental immunity in allowing access to or use of this data, makes no warranties as to the validity, and assumes no liability associated with the use or misuse of this information.


Legend

City Limits	Agricultural/Rural	Industrial
Interstate	Rural Residential	Central Business District
Principal Arterial	Urban Transition Residential	Community Business
Minor Arterial	Urban Residential	Public and Quasi-Public
Major Collector	Mixed-Use Residential	Military/Federal
Minor Collector	Mixed-Use Commercial	Open Space and Parks
Local	Mixed-Use Employment	
Private		
Platted not built		
Ownership		

(EXHIBIT "A")
**ANNEXATION MAPS FOR
VARIOUS COUNTY POCKETS SITUATE IN THE WEST 1/2 OF
SECTION 27, T. 14 N., R. 66 W., 6TH P.M.,
CITY OF CHEYENNE, LARAMIE COUNTY, WYOMING**




VICINITY MAP
NOT TO SCALE

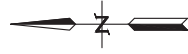

FILING RECORD

AZIMUTH

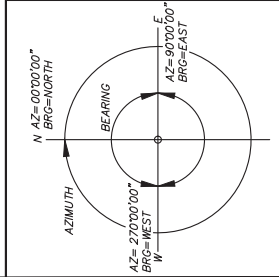

APPROVALS

APPROVED BY THE CITY COUNCIL OF THE CITY OF CHEYENNE, WYOMING, THIS
____ DAY OF _____, 2024.


ATTEST: _____
MAYOR – PATRICK COLLINS
CITY CLERK – KRISTINA F. JONES

NOTES

1. DISTANCES SHOWN ON THE ANNEXATION MAP ARE GROUND DISTANCE.
2. THE AREA WITHIN THE HEAVY BOUNDARY IS CURRENTLY A COUNTY POCKET. ALL AREAS OUTSIDE THE BOUNDARY ARE WITHIN THE LIMITS OF THE CITY OF CHEYENNE.
3. LENGTH OF THE PARCEL BOUNDARY ABUTTING THE CITY LIMITS – 23,726' (ALL SIDES OF THE PARCELS AS SHOWN ARE BOUNDED BY THE CITY LIMITS.
4. RATIO OF THE BOUNDARY ABUTTING THE CITY LIMITS – 100% OF THE TOTAL
5. CERTAIN POCKET PARCELS ARE DEPICTED FROM MAPS, PLATS AND DEEDS OF RECORD AND WERE NOT DETERMINED FROM ACTUAL FIELD SURVEYS.

SURVEYORS CERTIFICATE

I, COTTON D. JONES, A REGISTERED PROFESSIONAL LAND SURVEYOR IN THE STATE OF WYOMING, HEREBY STATE THAT THESE ANNEXATION MAPS WERE PREPARED FROM OFFICIAL PLATS AND DEEDS OF RECORD AND/OR FROM NOTES OF A FIELD SURVEY CONDUCTED BY MYSELF AND UNDER MY DIRECT SUPERVISION DURING THE MONTHS OF MAY–JUNE, 2024, THAT THE MONUMENTS ARE SET OR FOUND AS SHOWN AND THAT THESE MAPS CORRECTLY REPRESENT SAID SURVEYS AND MAP AND DEED DESCRIPTIONS OF THE LANDS DEPICTED HEREON TO THE BEST OF MY KNOWLEDGE.

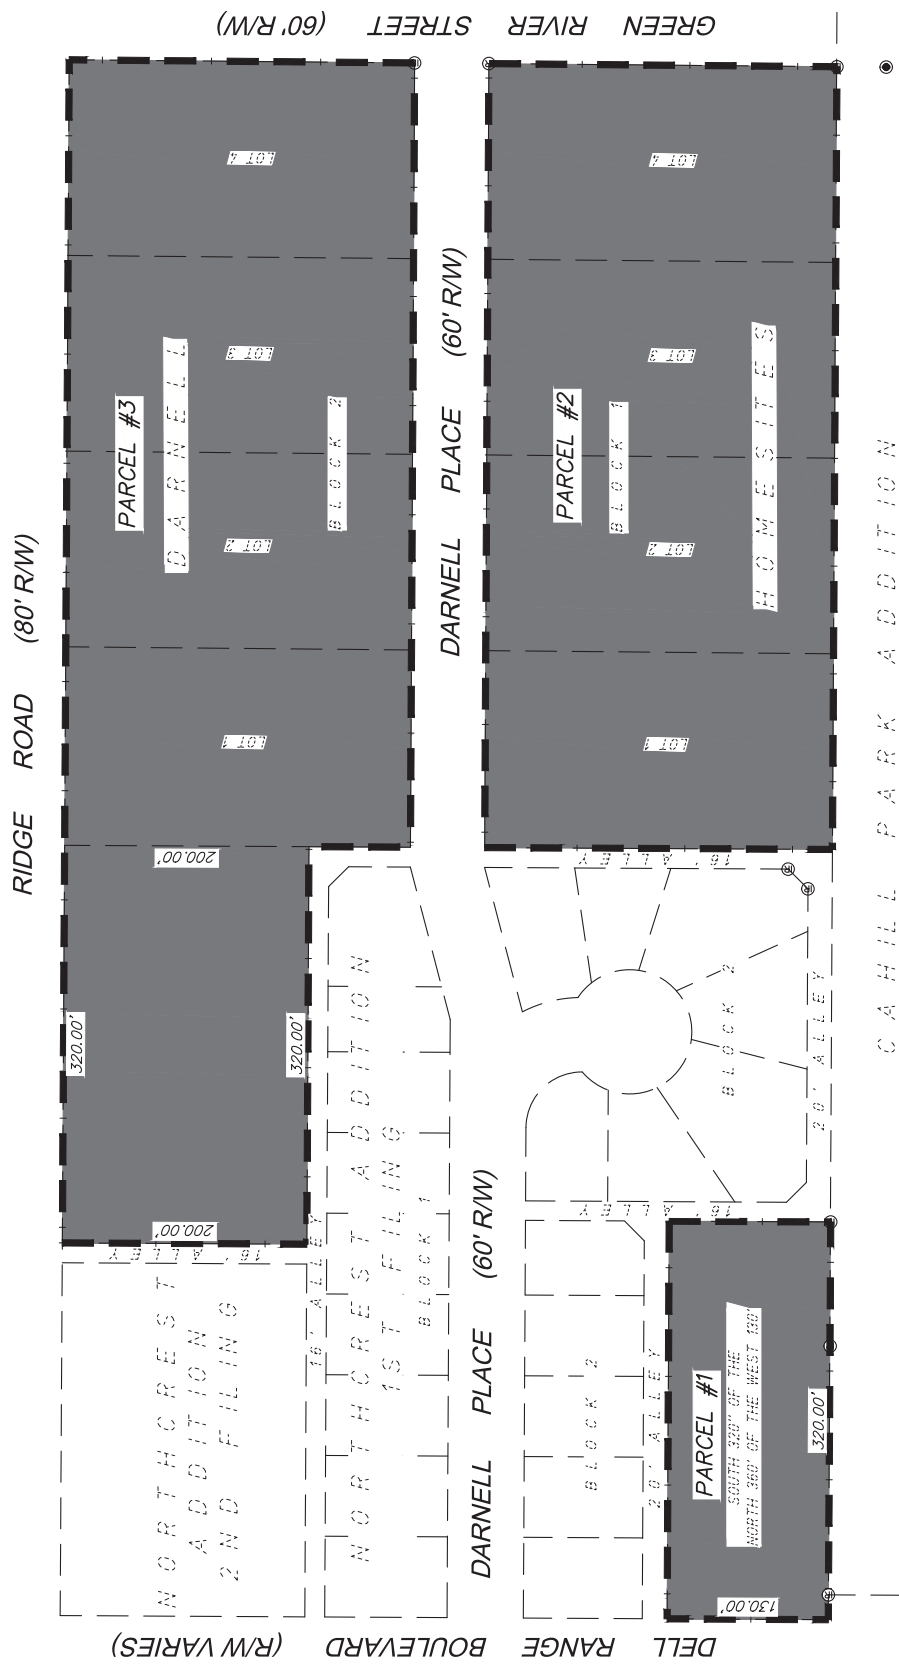

LAND DESCRIPTION

PARCELS OF LAND SITUATE IN NW $\frac{1}{4}$ NW $\frac{1}{4}$, SECTION 27, T. 14 N., R. 66 W., 6TH P.M., LARAMIE COUNTY, WYOMING, BEING MORE PARTICULARLY DESCRIBED AS FOLLOWS:



PARCEL #1 - SOUTH 320' OF THE NORTH 360' OF THE WEST 130' OF SAID SECTION 27

PARCEL #2 - ALL OF LOTS 1-4, BLOCK 1, DARNELL HOMESITES.


PARCEL #3 - ALL OF LOTS 1-4, BLOCK 2, DARNELL HOMESITES TOGETHER A THAT PORTION OF THE NW $\frac{1}{4}$ NW $\frac{1}{4}$, SECTION 27 LYING EAST OF RIDGE ROAD RIGHT-OF-WAY, SOUTH OF NORTHCREST, 2ND FILING, EAST OF NORTHCREST, 1ST FILING AND NORTH OF LOT 1, BLOCK 2, DARNELL HOMESITES. PARCEL DIMENSIONS ARE 200' EAST-WEST AND 320' NORTH-SOUTH.


SAID PARCELS CONTAIN 10.49 ACRES MORE OR LESS.

- LEGEND**
- PROPOSED AREA FOR ANNEXATION
 - EXISTING CITY LIMITS
 - FOUND 1" PLASTIC CAP
 - FOUND STANDARD WYDOT RIGHT-OF-WAY MONUMENT
 - FOUND ALUMINUM CAP
 - FOUND #5 REBAR

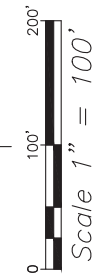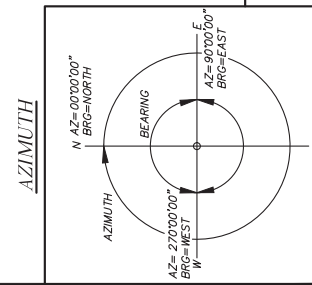


FILING RECORD


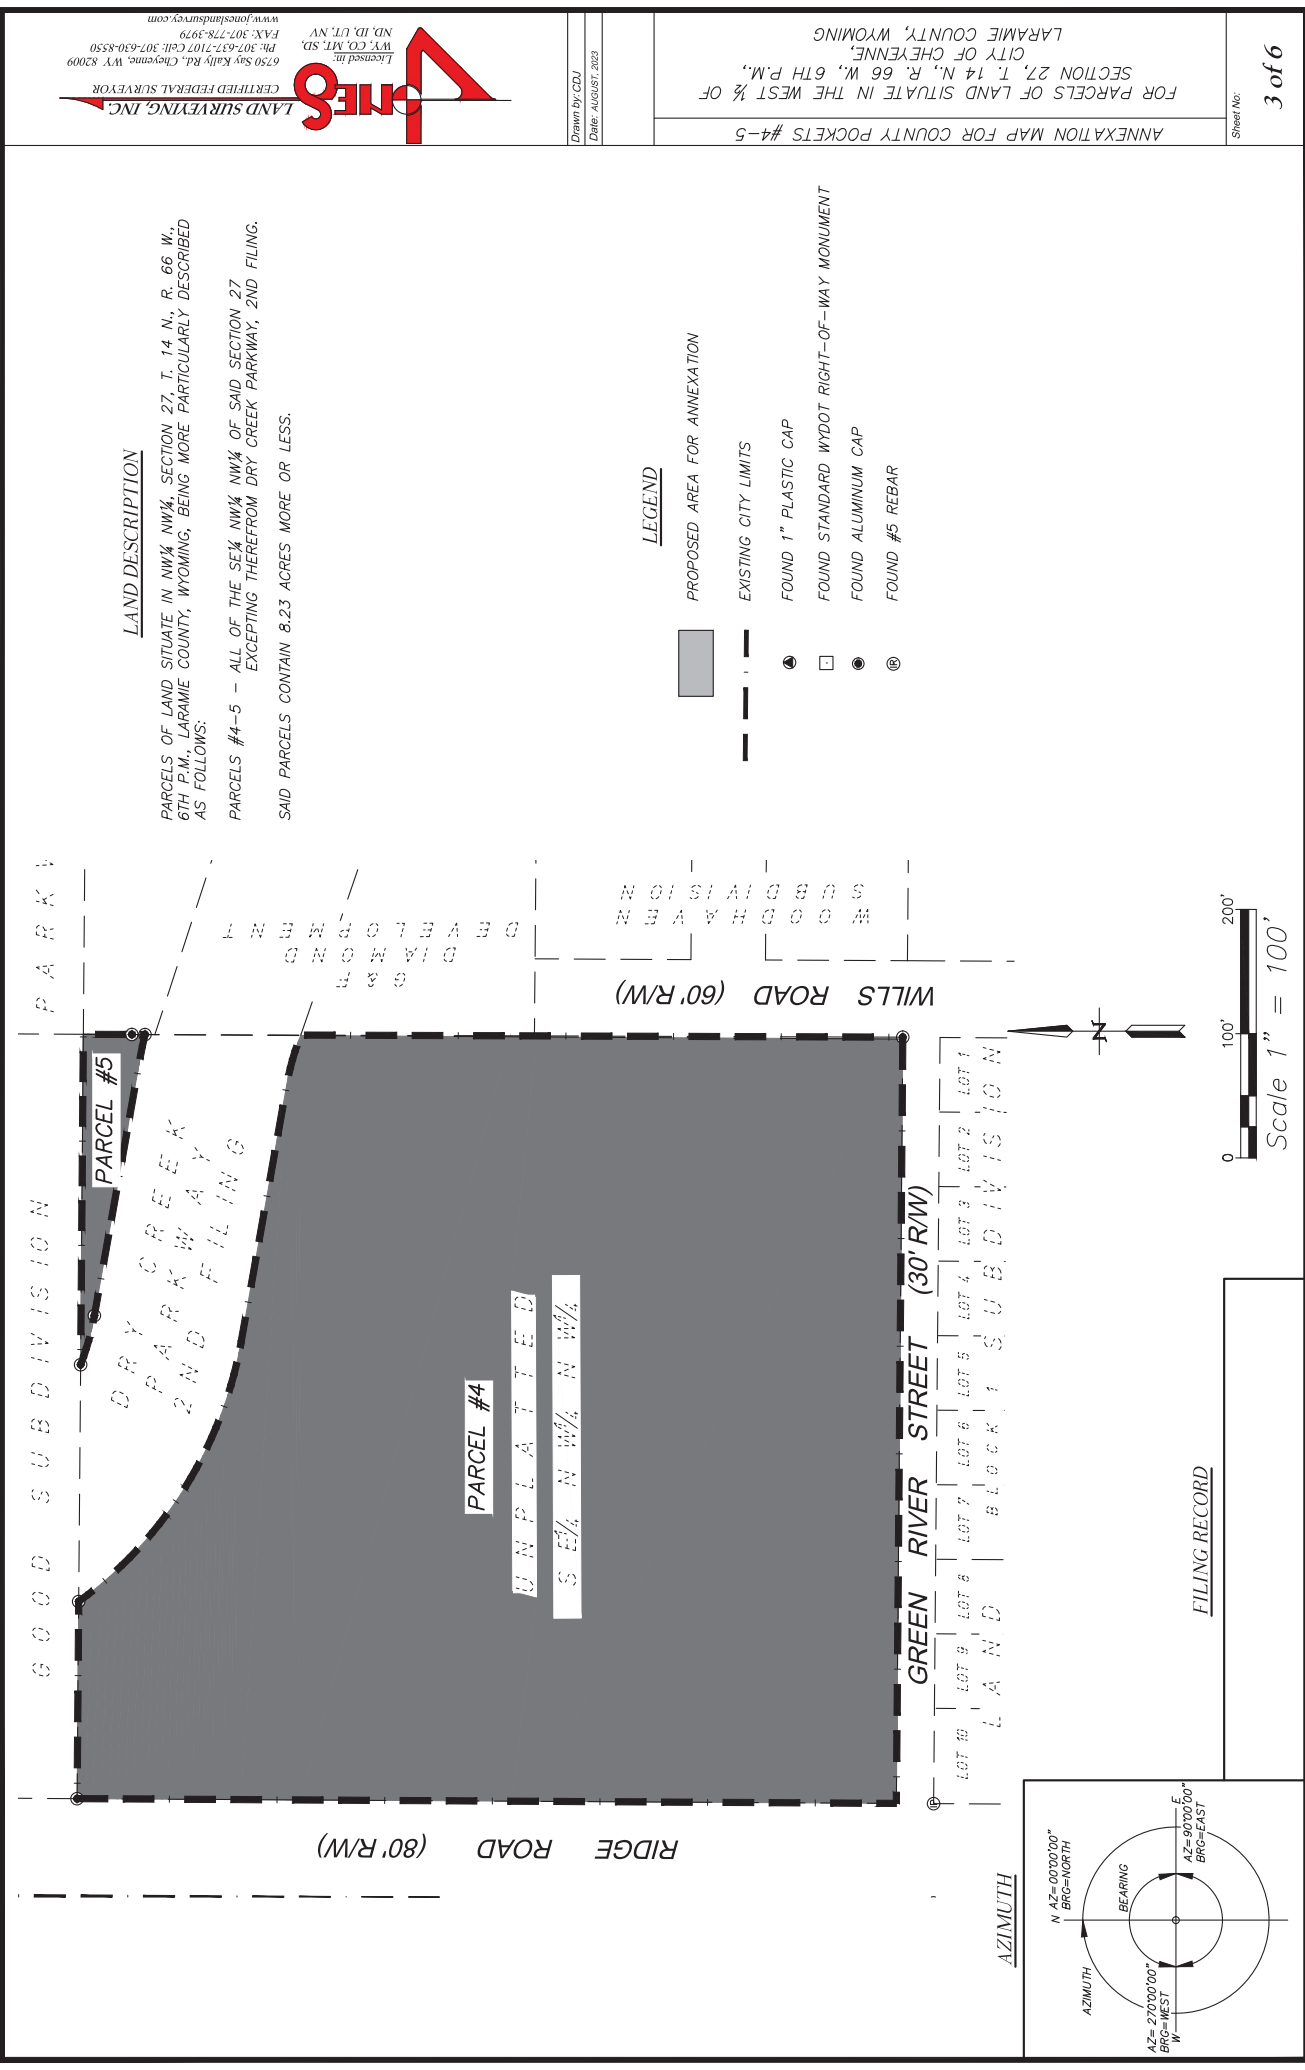


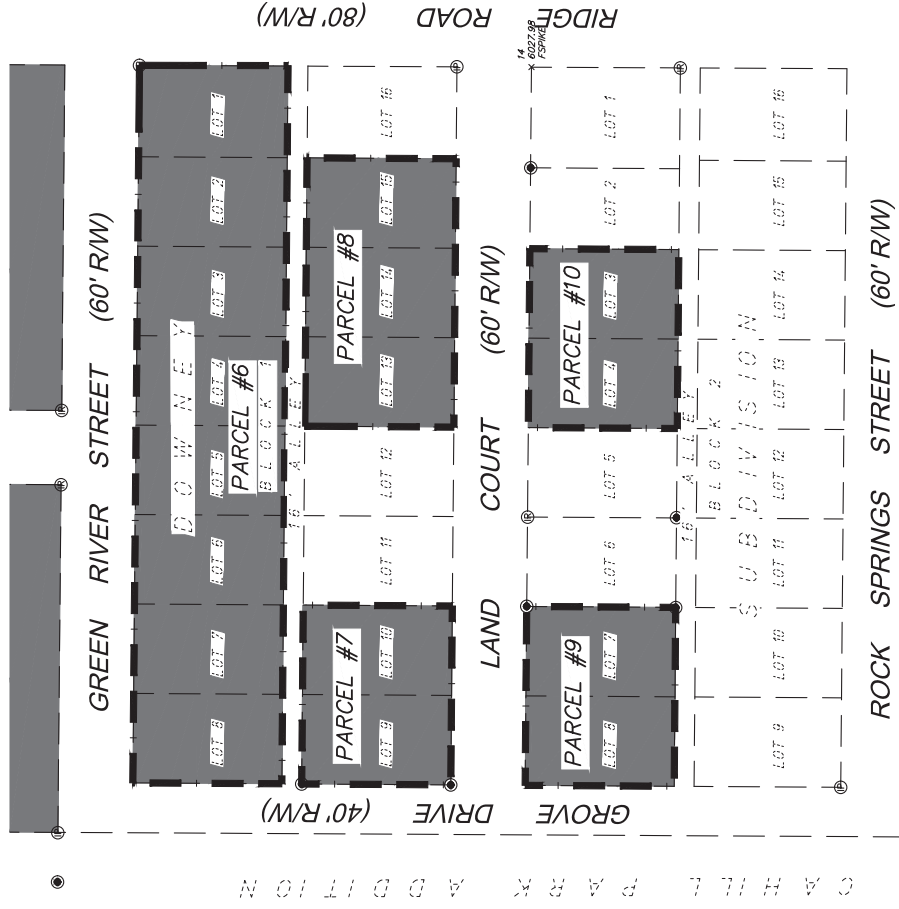

AZIMUTH

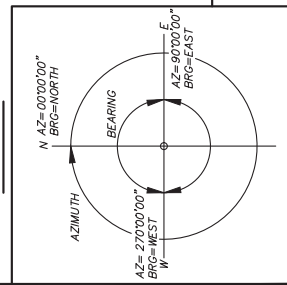

FILING RECORD

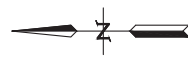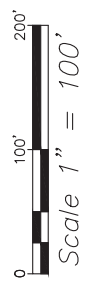

LEGEND

- PROPOSED AREA FOR ANNEXATION
- EXISTING CITY LIMITS
- FOUND 1" PLASTIC CAP
- FOUND STANDARD WYDOT RIGHT-OF-WAY MONUMENT
- FOUND ALUMINUM CAP
- FOUND #5 REBAR

LAND DESCRIPTIONS

PARCELS OF LAND SITUATE IN NW¼ NW¼, SECTION 27, T. 14 N., R. 66 W., 6TH P.M., LARAMIE COUNTY, WYOMING, BEING MORE PARTICULARLY DESCRIBED AS FOLLOWS:

PARCELS #6 – ALL OF LOTS 1–8, BLOCK 1, DOWNEY SUBDIVISION.


PARCELS #7 – ALL OF LOTS 9–10, BLOCK 1, DOWNEY SUBDIVISION.

PARCELS #8 – ALL OF LOTS 13–15, BLOCK 1, DOWNEY SUBDIVISION.


PARCELS #9 – ALL OF LOTS 7–8, BLOCK 2, DOWNEY SUBDIVISION.

PARCELS #10 – ALL OF LOTS 3–4, BLOCK 2, DOWNEY SUBDIVISION.



SAID PARCELS CONTAIN 3.37 ACRES MORE OR LESS.

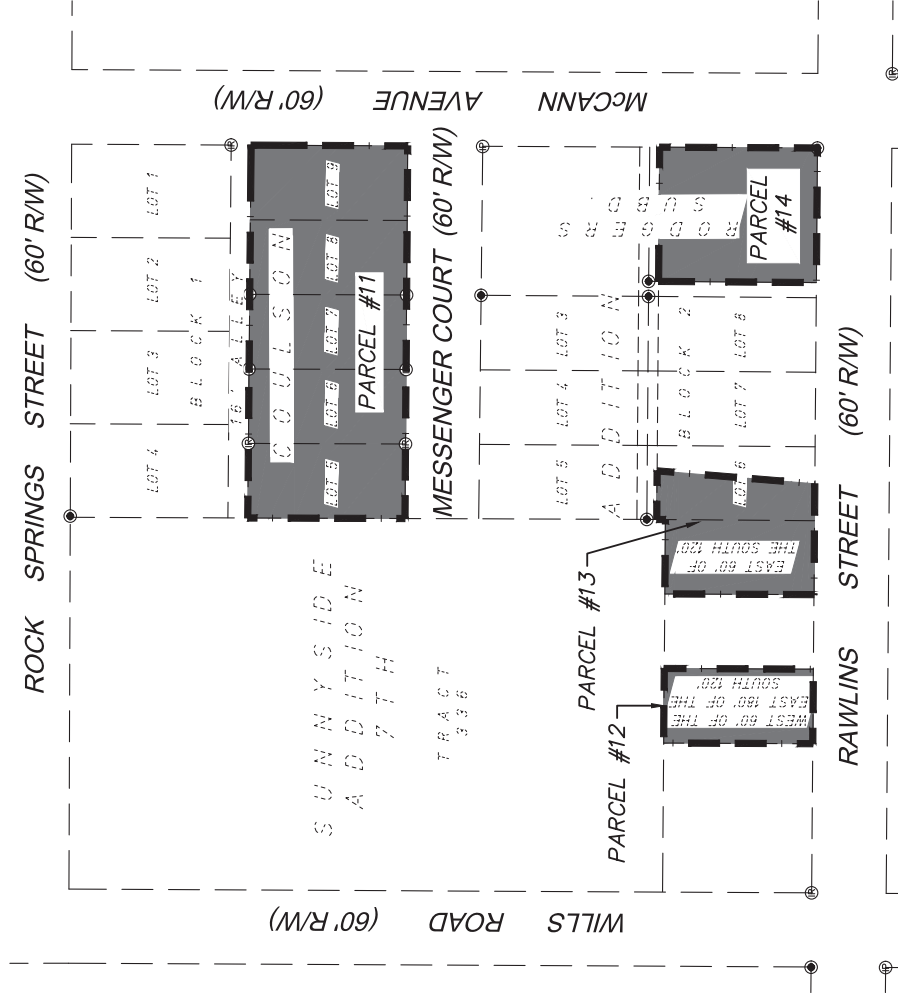

RAWLINS STREET (60' R/W)

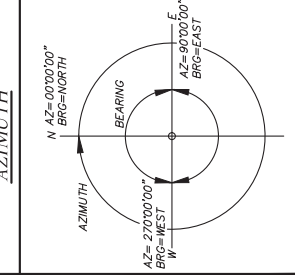

FILING RECORD

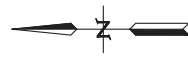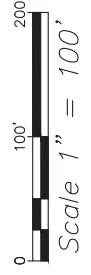

LAND DESCRIPTION

PARCELS OF LAND SITUATE IN SE¼ NW¼, SECTION 27, T. 14 N., R. 66 W., 6TH P.M., LARAMIE COUNTY, WYOMING, BEING MORE PARTICULARLY DESCRIBED AS FOLLOWS:

PARCELS #11 – ALL OF LOTS 5–9, BLOCK 1, COULSON ADDITION.

PARCELS #12 – THE WEST 60 FEET OF THE EAST 180 FEET OF THE SOUTH 120 FEET, TRACT 336, SUNNYSIDE ADDITION, 7TH FILING.


PARCELS #13 – THE EAST 60 FEET OF THE SOUTH 120 FEET, TRACT 336, SUNNYSIDE ADDITION, 7TH FILING TOGETHER WITH A PORTION OF TRACT 6, BLOCK 2, COULSON ADDITION DESCRIBED AS BEGINNING AT THE SOUTHWEST CORNER OF SAID LOT 6, THENCE 00°19'20" A DISTANCE OF 126.80 FEET; THENCE OF 90°26'01" A DISTANCE OF 39.74 FEET; THENCE 184°34'39" A DISTANCE OF 135.185 FEET; THENCE 270°28'12" A DISTANCE OF 29.71 FEET TO THE POINT OF BEGINNING.

PARCELS #14 – THE SOUTH 126.82 FEET OF LOT 1, BLOCK 1, RODGERS SUBDIVISION LYING SOUTH OF THE VACATED 16 FOOT ALLEY.

SAID PARCELS CONTAIN 1.62 ACRES MORE OR LESS.

LEGEND

- PROPOSED AREA FOR ANNEXATION
- EXISTING CITY LIMITS
- FOUND 1" PLASTIC CAP
- FOUND STANDARD WYDOT RIGHT-OF-WAY MONUMENT
- FOUND ALUMINUM CAP
- FOUND #5 REBAR

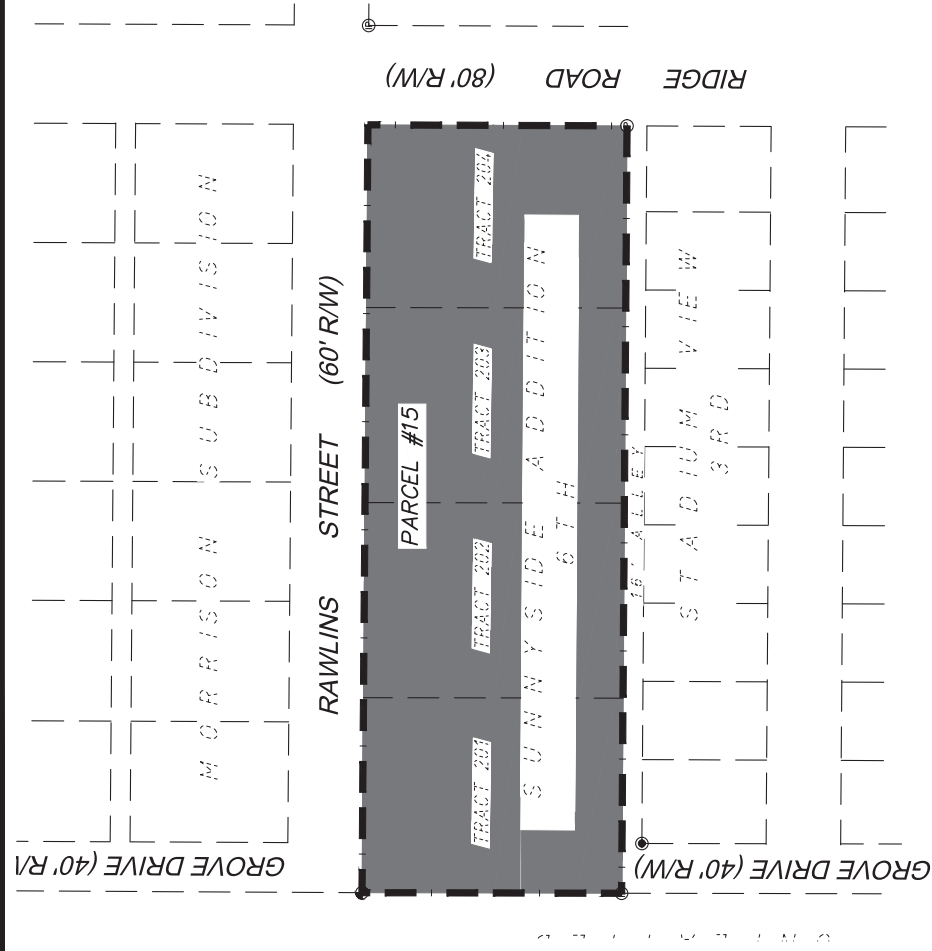

LAND DESCRIPTION

PARCELS OF LAND SITUATE IN NW¼ SW¼, SECTION 27, T. 14 N., R. 66 W., 6TH P.M., LARAMIE COUNTY, WYOMING, BEING MORE PARTICULARLY DESCRIBED AS FOLLOWS:

PARCELS #15 - THE NORTH 209.45 FEET OF TRACTS 201-204, SUNNYSIDE ADDITION, 6TH FILING EXCEPTING THEREFROM THE EAST 10.00 FEET OF THE NORTH 209.45 OF TRACT 204, SUNNYSIDE ADDITION, 6TH FILING.

SAID PARCELS CONTAIN 2.96 ACRES MORE OR LESS.

LEGEND

PROPOSED AREA FOR ANNEXATION

EXISTING CITY LIMITS


FOUND 1" PLASTIC CAP

FOUND STANDARD WYDOT RIGHT-OF-WAY MONUMENT

FOUND ALUMINUM CAP

FOUND #5 REBAR

AZIMUTH

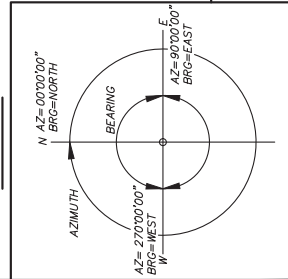

FILING RECORD

Scale 1" = 100'

Sheet No.

6 of 6

FOR PARCELS OF LAND SITUATE IN THE NW¼ SW¼ OF SECTION 27, T. 14 N., R. 66 W., 6TH P.M., LARAMIE COUNTY, WYOMING, CITY OF CHEYENNE.

ANNEXATION MAP FOR COUNTY POCKET #15

Drawn by: CDJ
Date: AUGUST, 2023

LAND SURVEYING, INC.
CERTIFIED FEDERAL SURVEYOR
6750 Sky Kally Rd., Cheyenne, WY 82009
Ph: 307-637-7107 Cell: 307-630-8550
FAX: 307-778-3979
www.jonesslandsurvey.com

Joness
Licensed in
WY, CO, MT, SD,
ND, ID, UT, NV

